



AMTRAK BEECHGROVE

10.41.33.0/24

C9200L-48P-4X
10.41.33.142

MRSAMTRBFEIN09S02

C9200L-24P-4X
10.41.33.153

MRSAMTRBFEIN09S08

C9200L-48P-4X
10.41.33.149

MRSAMTRBFEIN09S04

C9200L-48P-4X
10.41.33.140

MRSAMTRBFEIN09S20

C9200L-48P-4X
10.41.33.141

MRSAMTRBFEIN09S21

C9200L-48P-4X
10.41.33.150

MRSAMTRBFEIN09S06

C9200L-48P-4X
10.41.33.146

MRSAMTRBFEIN09S30

C9200L-48P-4X
10.41.33.151

MRSAMTRBFEIN09S07

C9200L-24P-4X
10.41.33.144

MRSAMTRBFEIN09S29

Te1/1/1

Te1/1/3

C9200L-24P-4X
10.41.33.157

MRSAMTRBFEIN09S11

C9200L-48P-4X
10.41.33.132

MRSAMTRBFEIN09S12

C9200L-24P-4X
10.41.33.147

MRSAMTRBFEIN09S03

Gi1/0/24

Gi1/0/23

C9200L-24P-4G
10.41.33.139

MRSAMTRBFEIN09S17

C9200L-48P-4X
10.41.33.133

MRSAMTRBFEIN09S13

C9200L-48P-4X
10.41.33.152

MRSAMTRBFEIN09S24

C9200L-24P-4X
10.41.33.143

MRSAMTRBFEIN09S27

C9200L-48P-4X
10.41.33.159

MRSAMTRBFEIN09S32

C9200L-24P-4X
10.41.33.158

MRSAMTRBFEIN09S22

C9200L-48P-4X
10.41.33.137

MRSAMTRBFEIN09S26

C9200L-24P-4X
10.41.33.154

MRSAMTRBFEIN09S09

C9200L-24P-4X
10.41.33.156


MRSAMTRBFEIN09S10

C9200L-24P-4X
10.41.33.138

MRSAMTRBFEIN09S16



AMTRAK BEECHGROVE

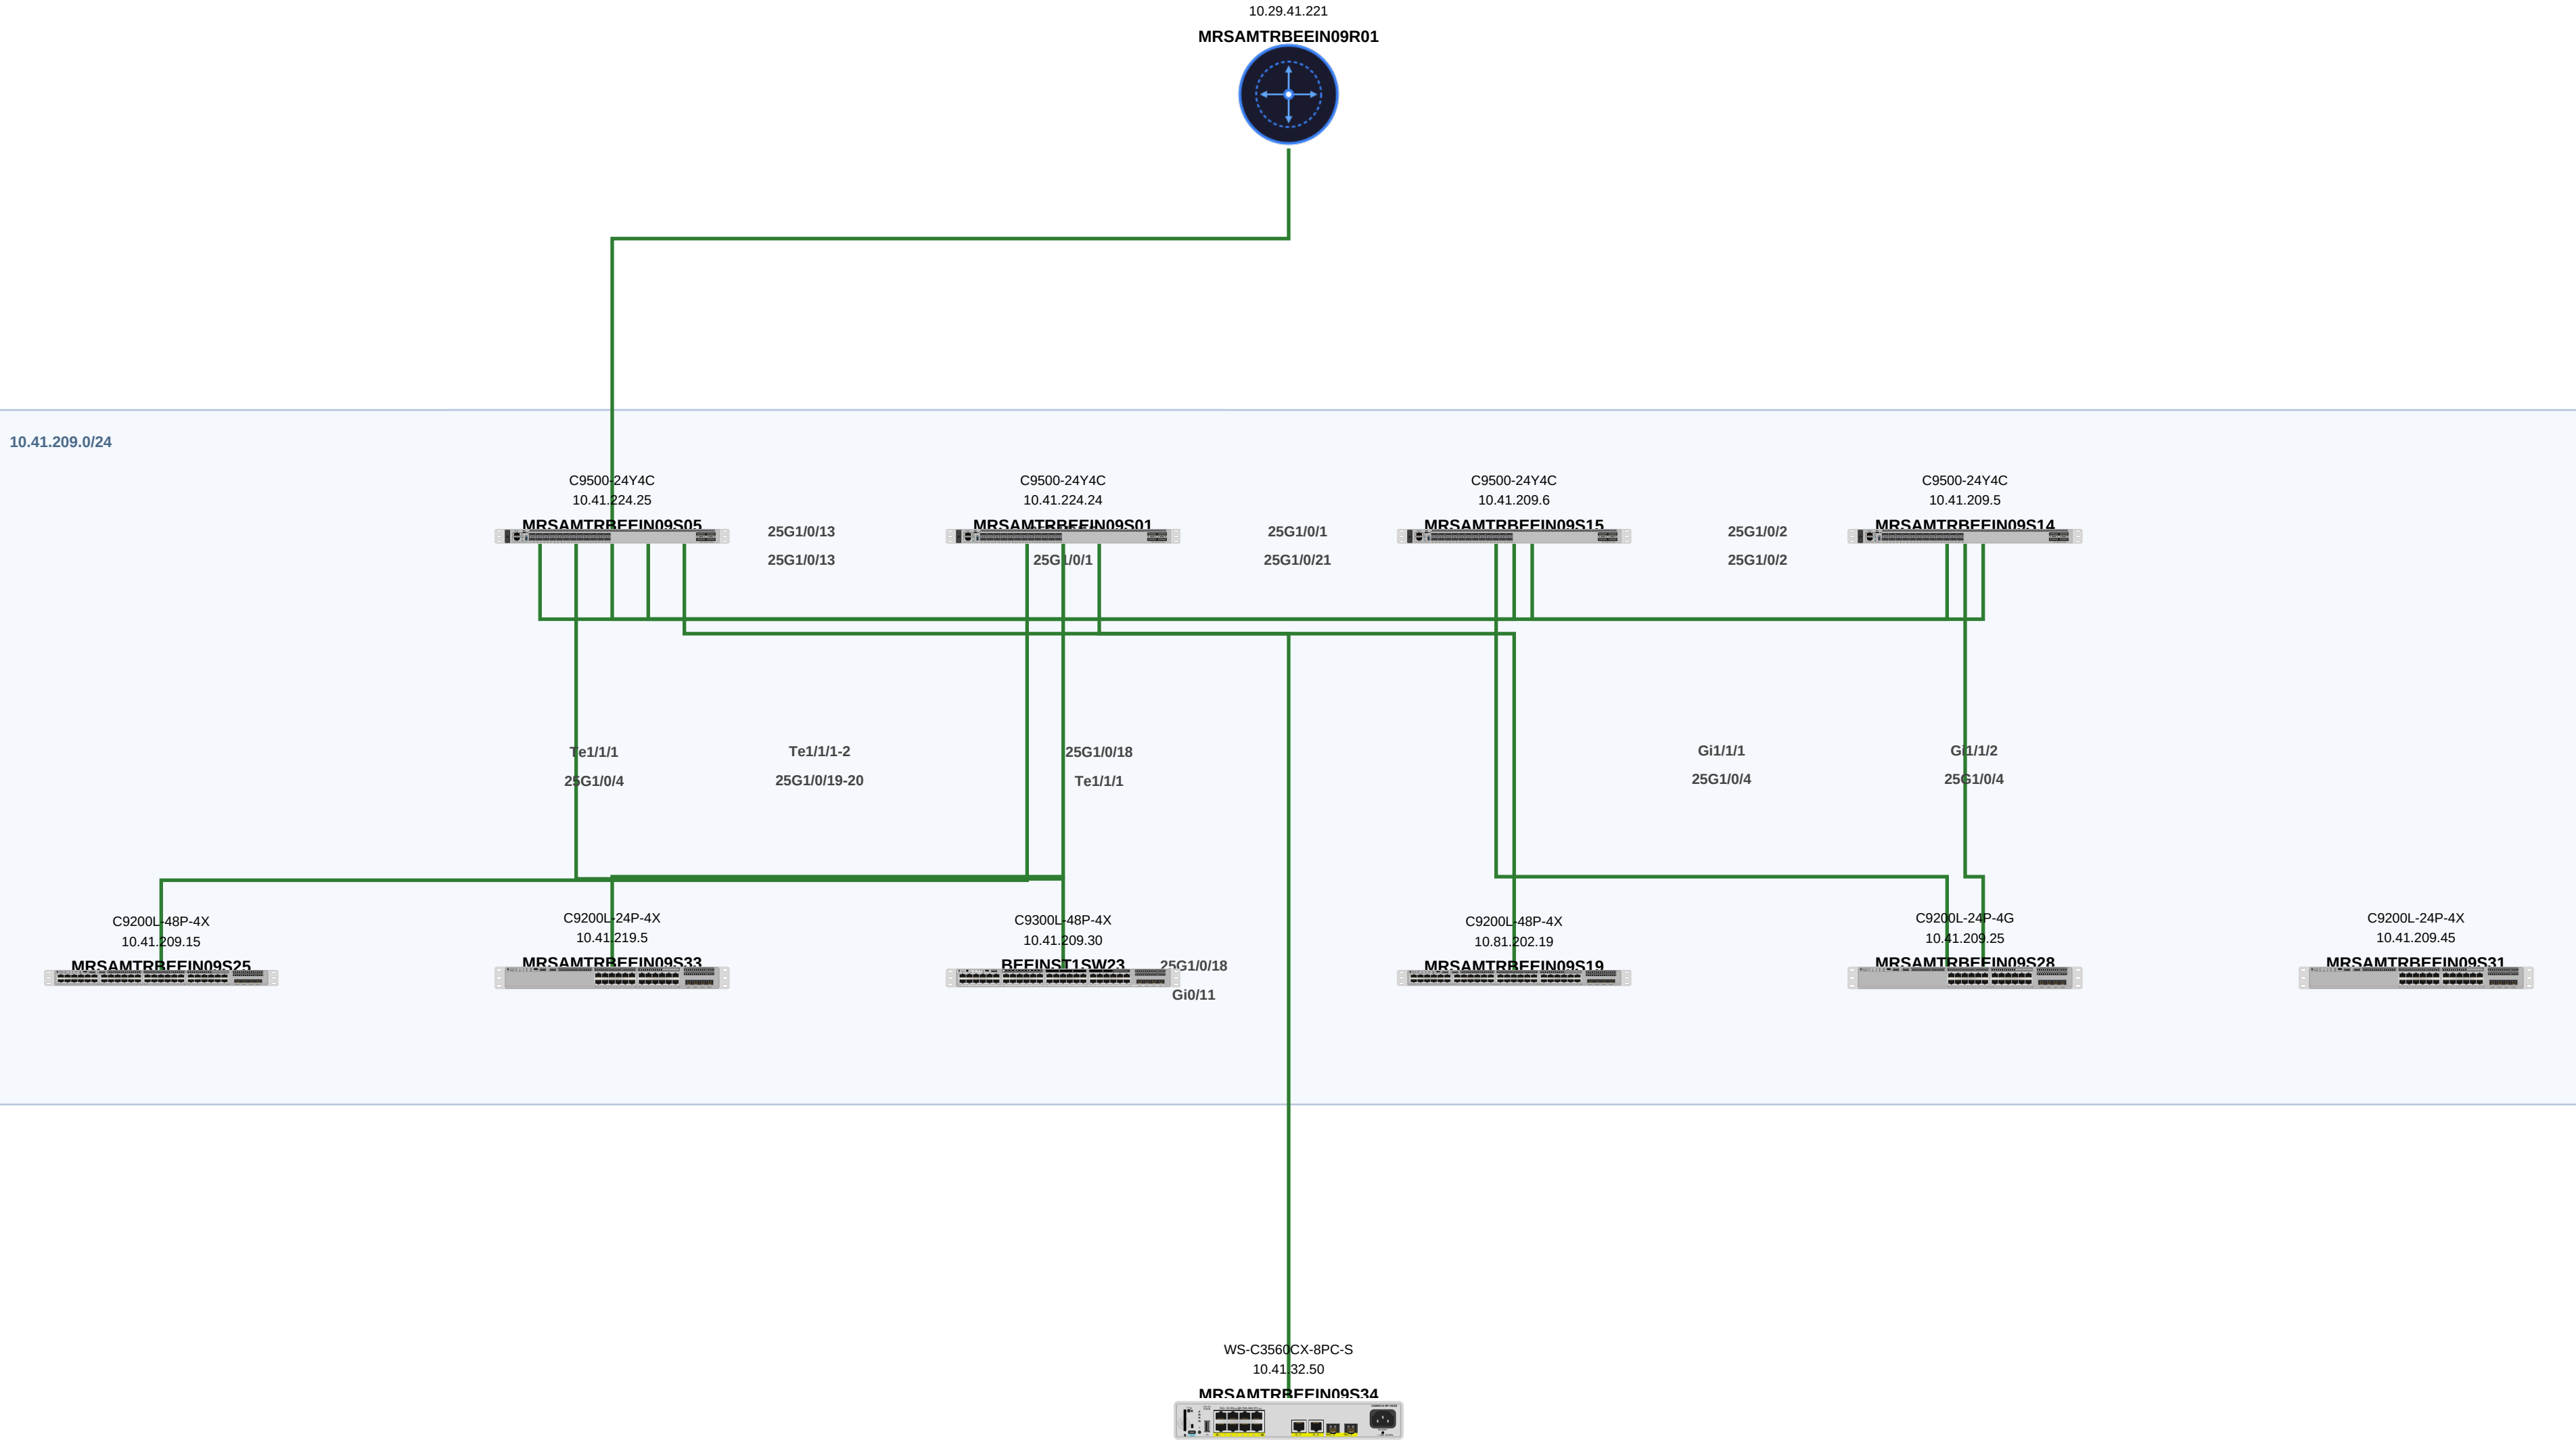



AMTRAK BEECHGROVE - ACCESS POINTS



LEGEND WAN / Internet Core Backbone LAN Fiber Management		Drawn By: NTS-Engineering		Drawn Date: 08142026	
		Drawing Title: AMTRAK BEECHGROVE			
		Document Name:			
		Revision: A		Rev. Date: 14 Aug 26	