



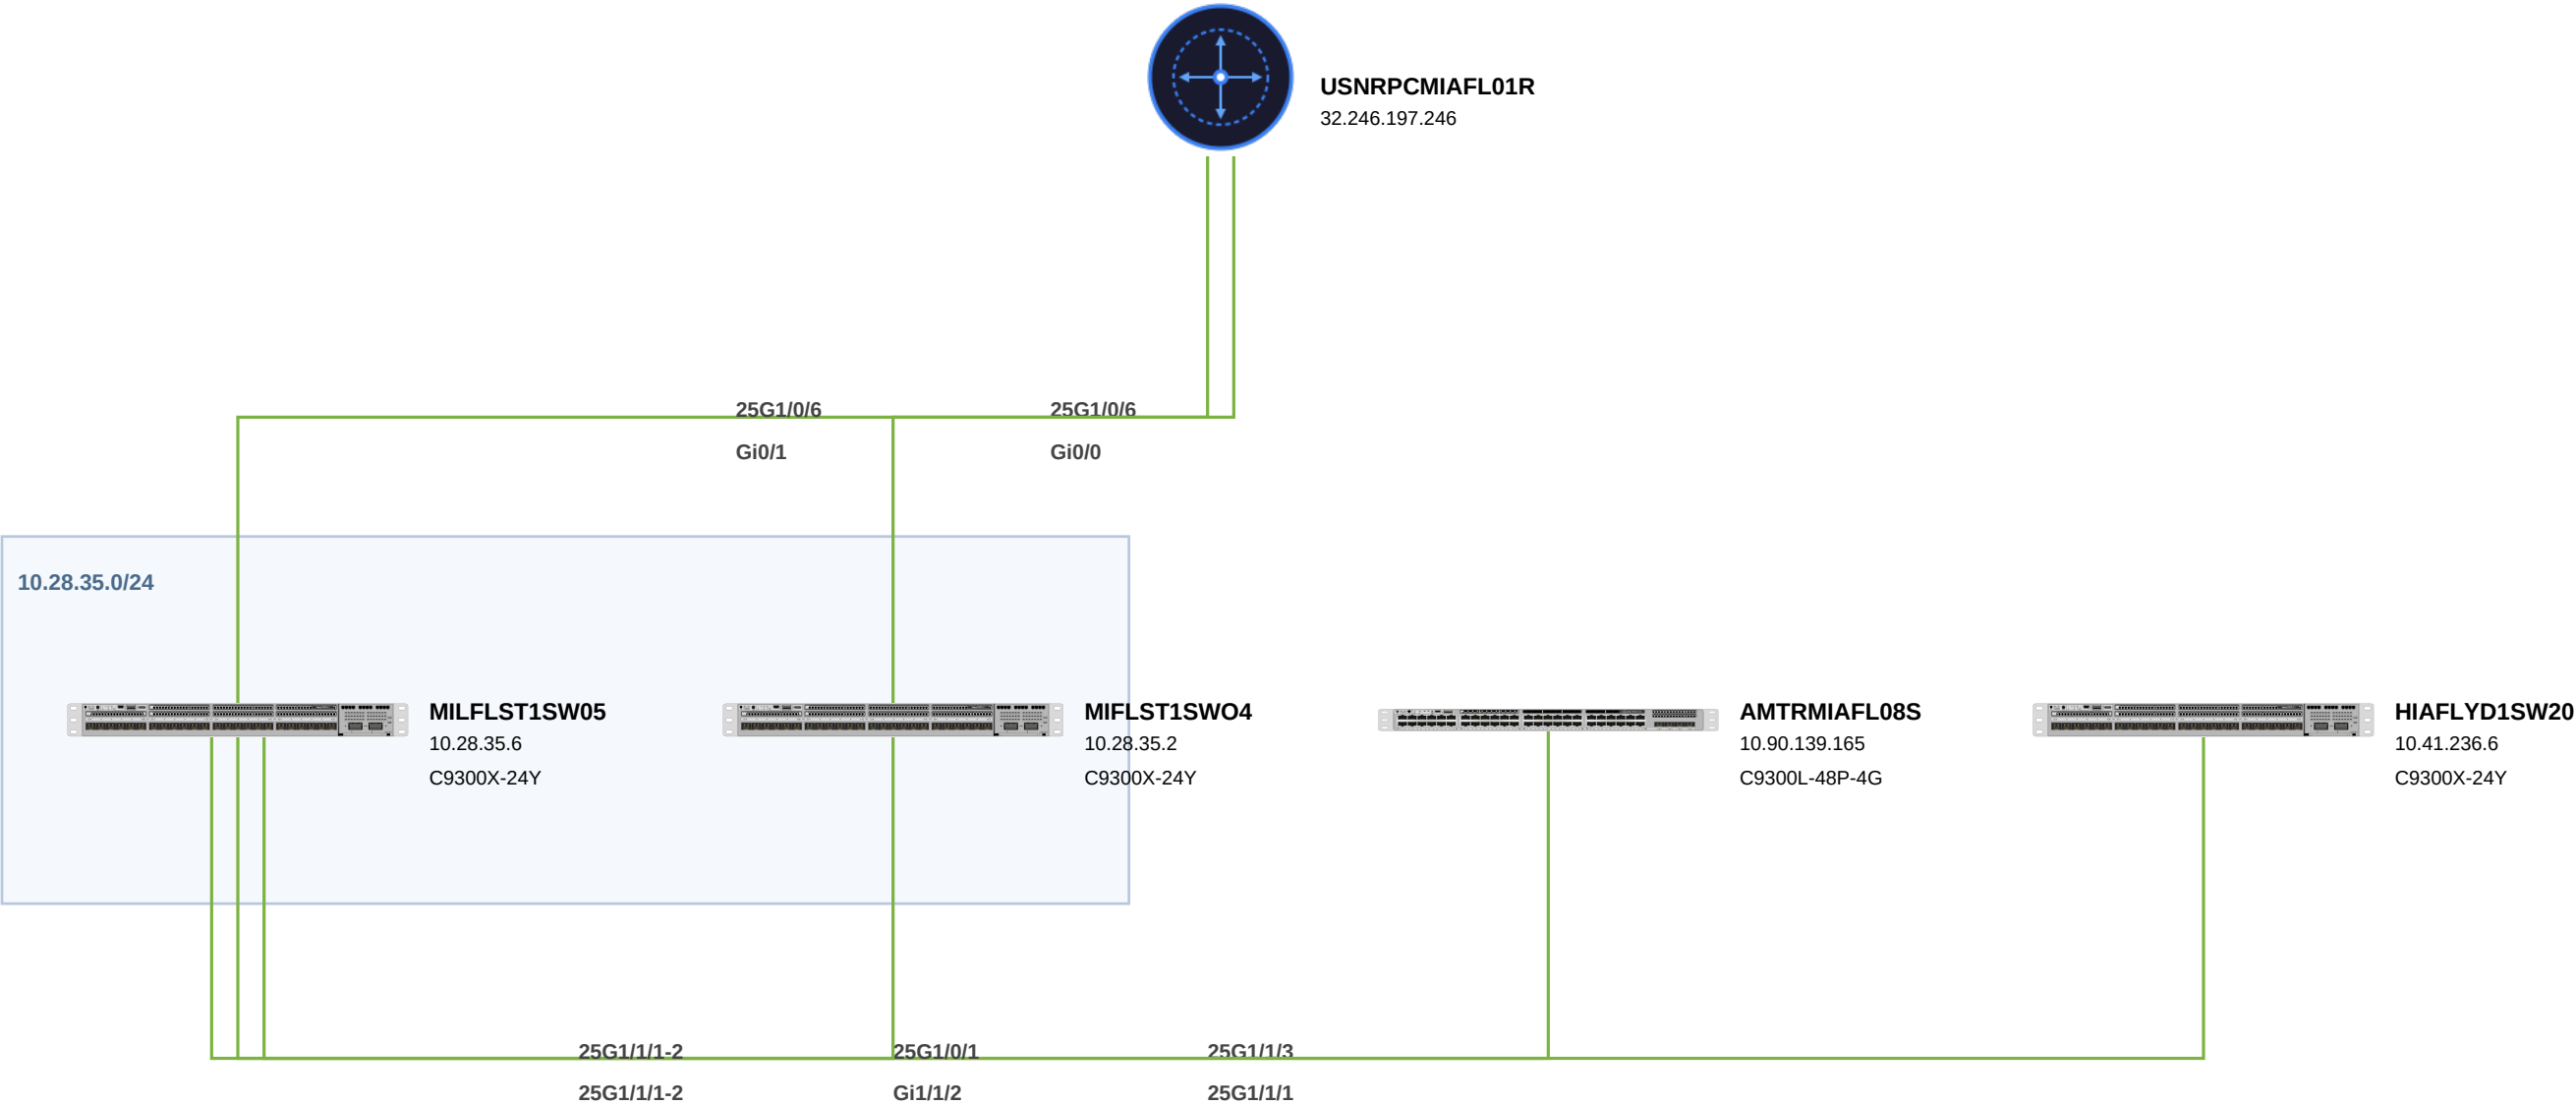

AMTRAK MIAMI

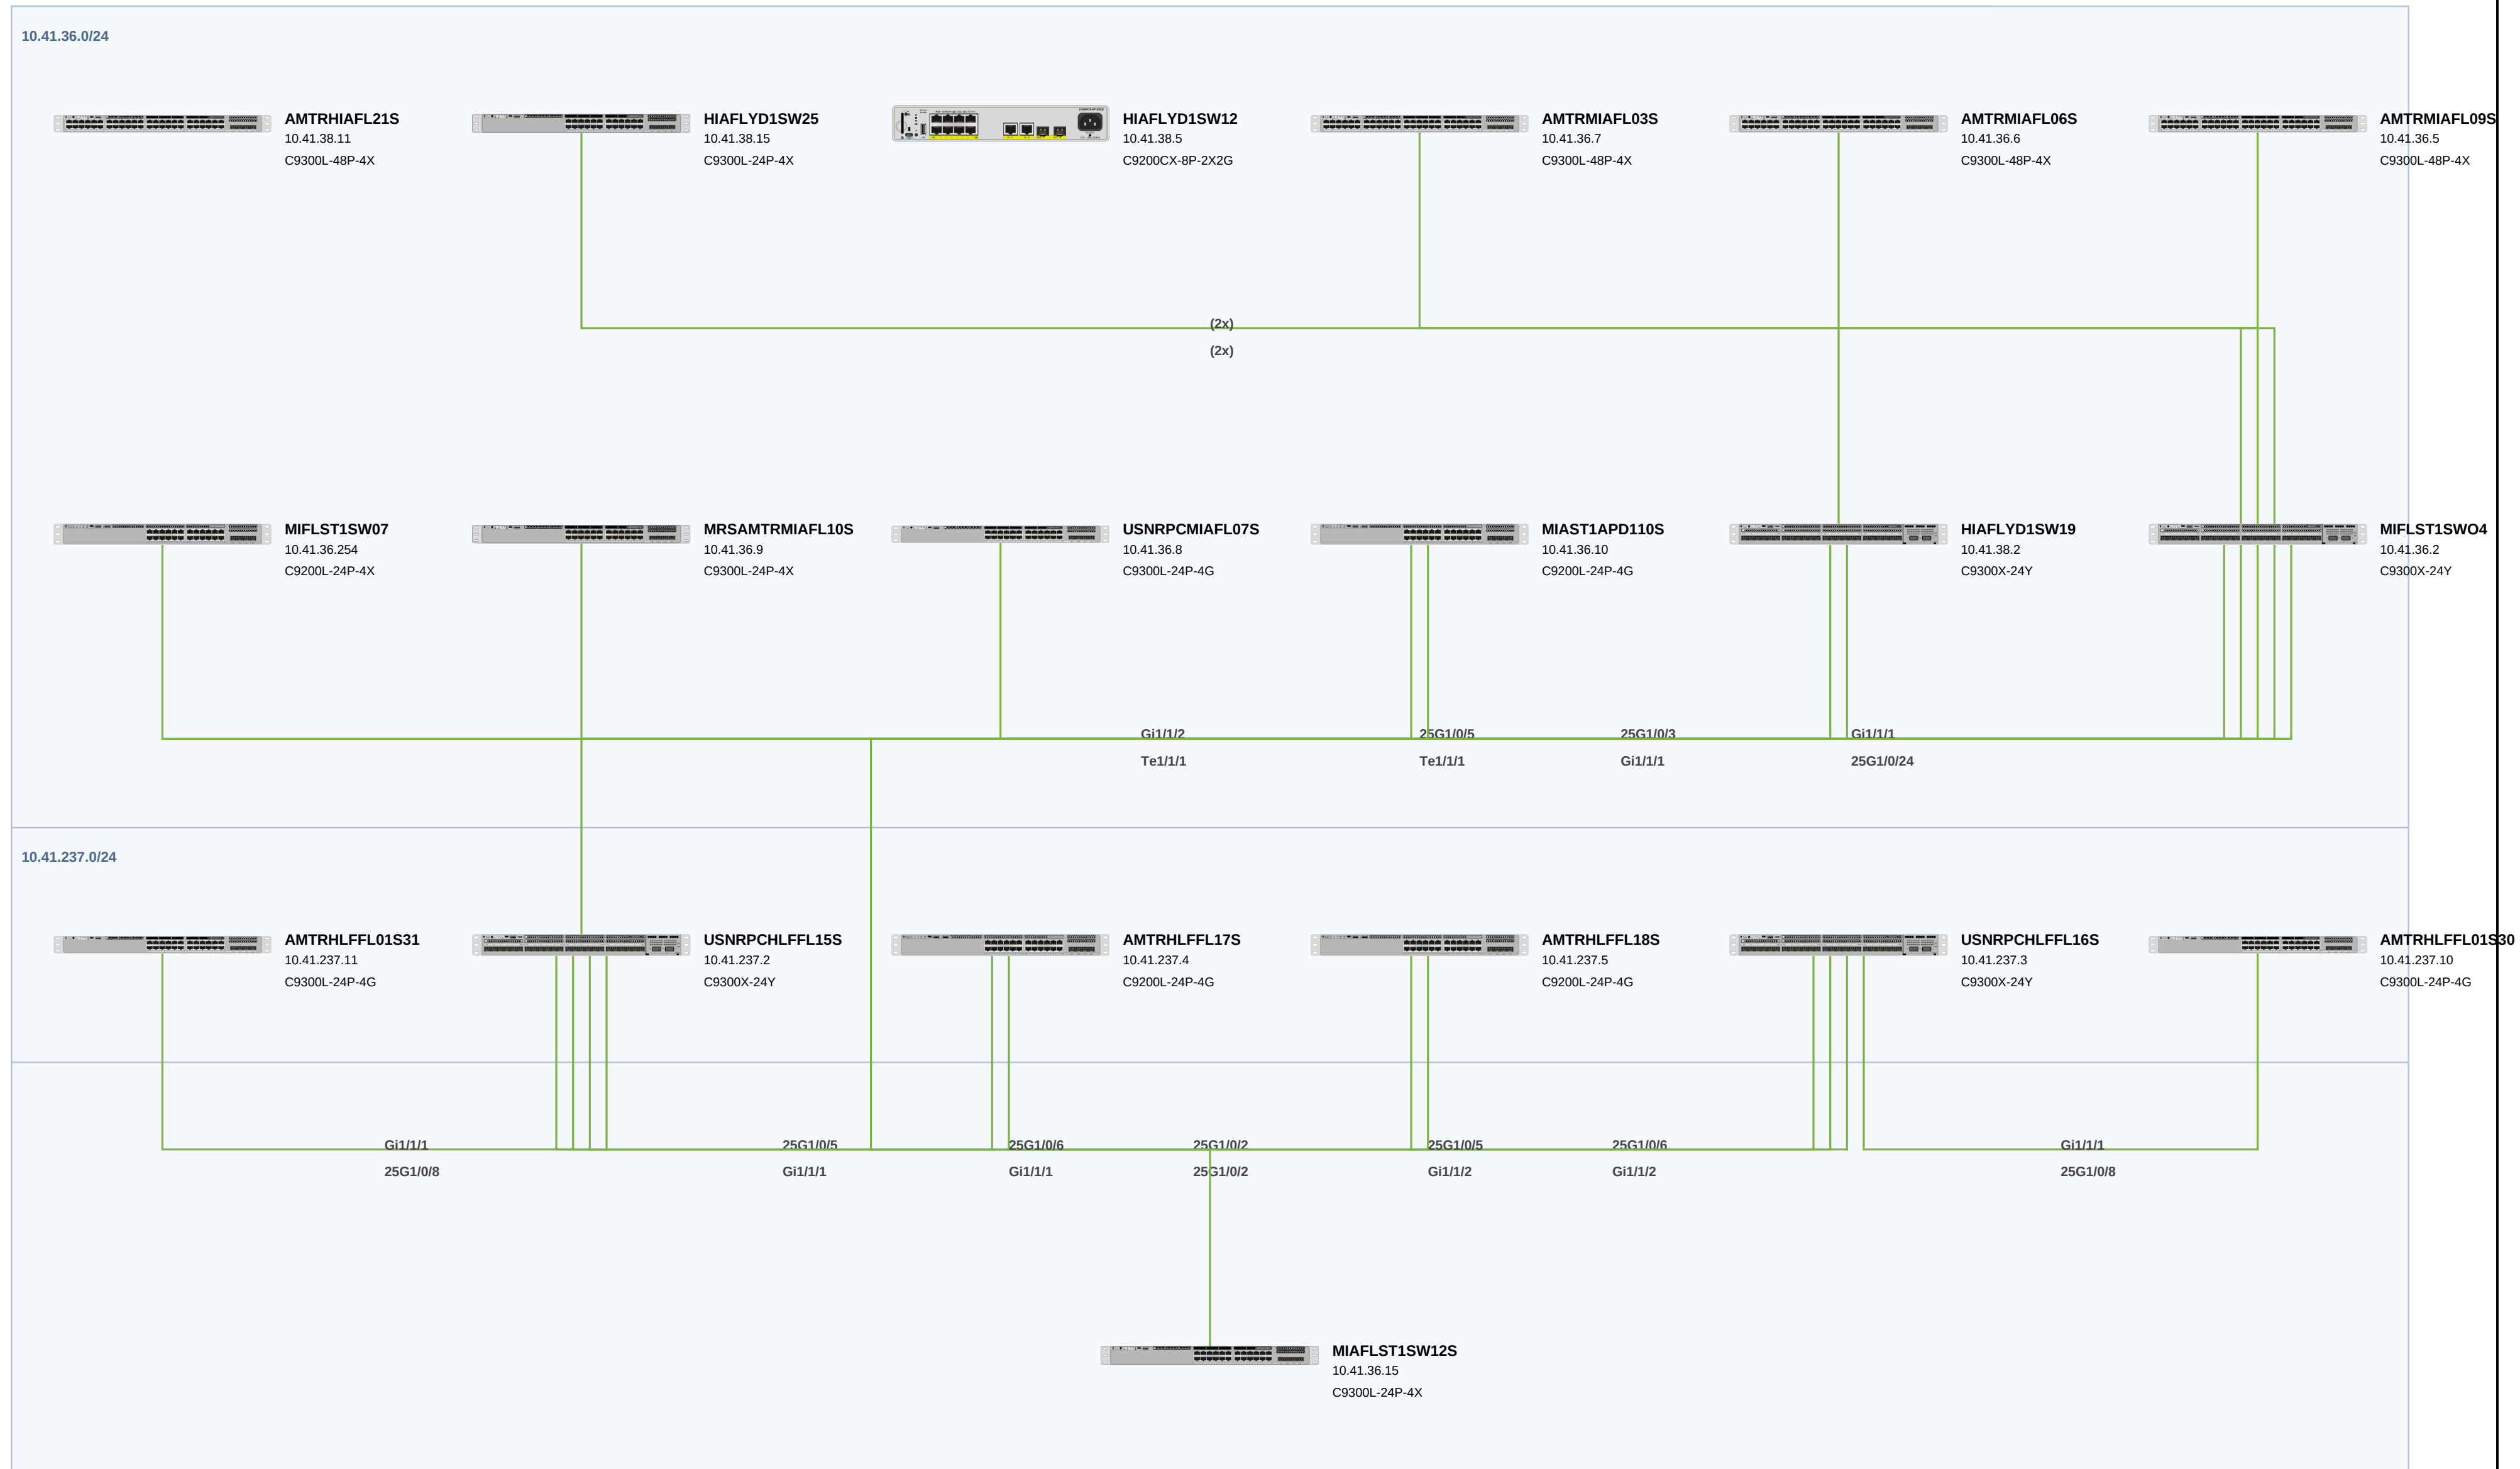





AMTRAK MIAMI - ACCESS POINTS



MIA-FL-AP09
10.241.106.21



MIAFLYD1AP03
10.241.39.35



MIAFLST1AP03
10.241.106.73



MIAFLYD1AP01
10.241.39.32



MIAFLYD1AP06
10.241.39.36



MIAFLYD1AP04
10.241.39.34



MIAFLYD1AP09
10.241.39.41



MIAFLYD1AP02
10.241.39.31



MIAFLYD1AP05
10.241.39.33



MIAFLYD1AP07
10.241.39.39



MIAFLYD1AP13
10.40.38.149



MIAFLYD1AP08
10.241.39.38



MIA-FL-AP10
10.241.106.31

LEGEND WAN / Internet Core Backbone LAN Fiber Management		Drawn By: NTS-Engineering		Drawn Date: 08142026	
		Drawing Title: AMTRAK MIAMI			
		Document Name:			
		Revision: A		Rev. Date: 14 Aug 26	