


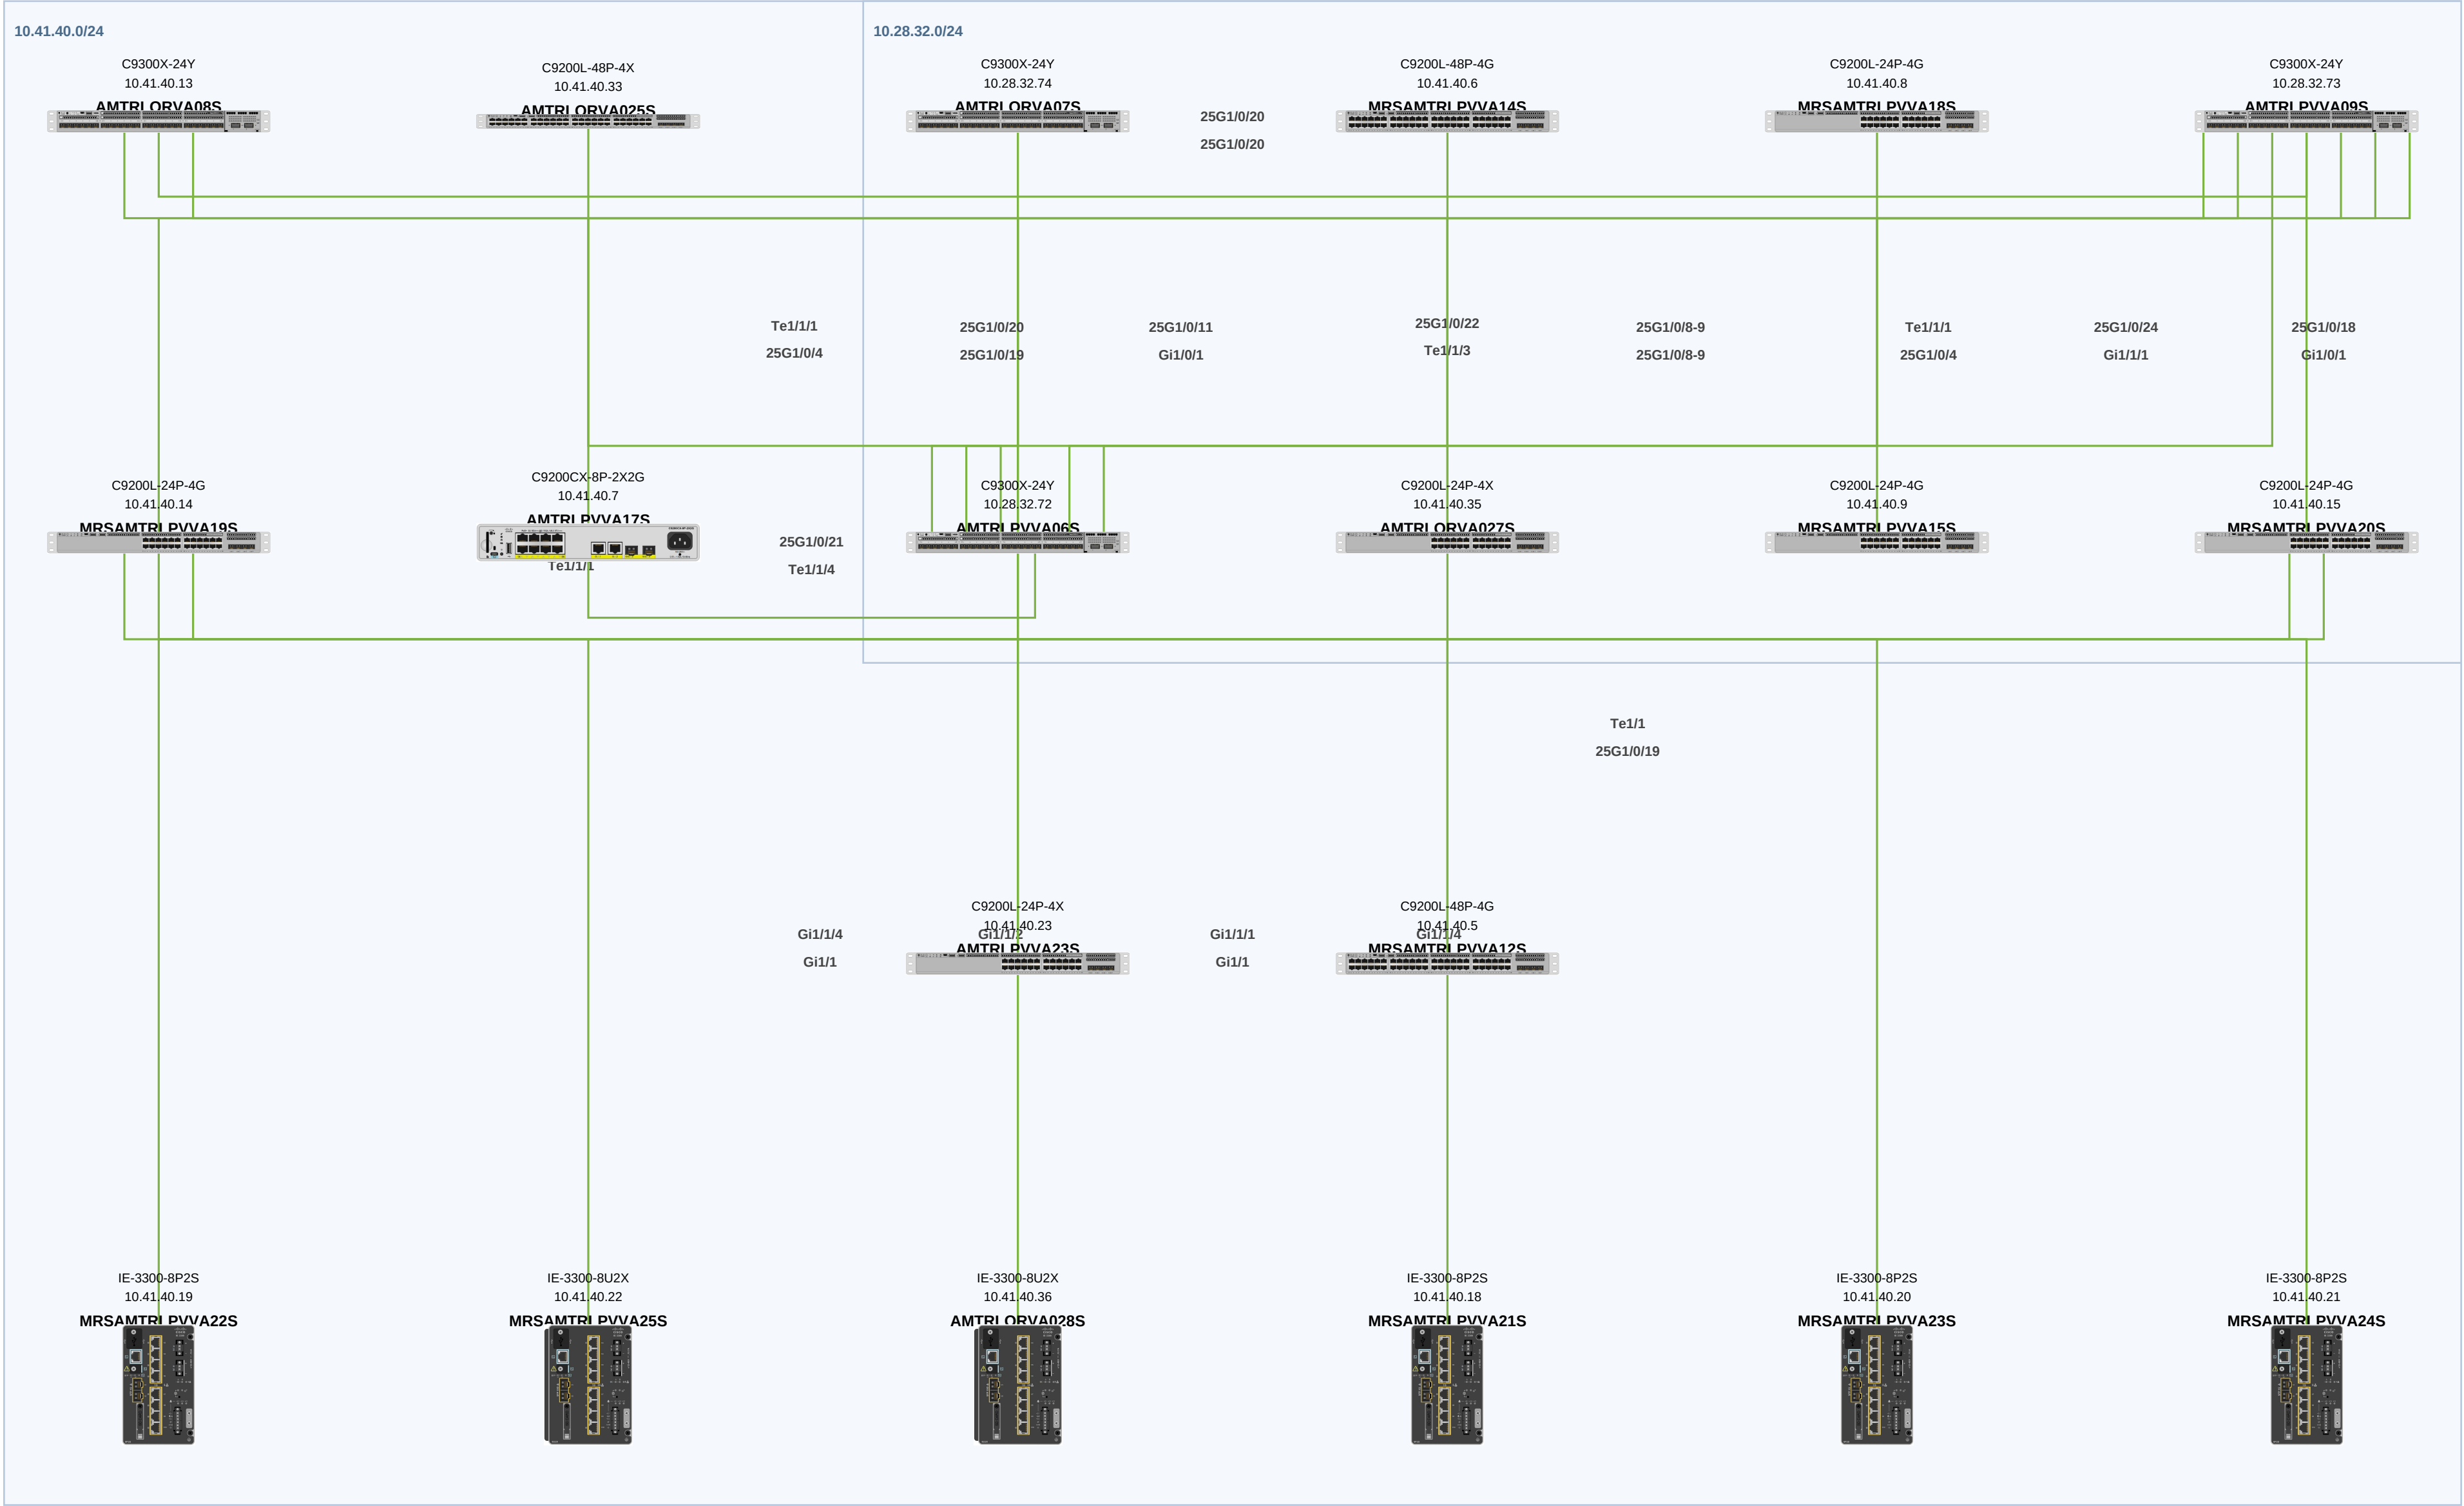

LORTON LOGICAL INFRASTRUCTURE



LEGEND WAN / Internet Core Backbone LAN Fiber Management	 AMTRAK - Proprietary Use Pursuant to Company Instructions	Drawn By:		Drawn Date: 08152026	
		Drawing Title: LORTON LOGICAL INFRASTRUCTURE			
		Document Name:			
		Revision:		Rev. Date: 14 Aug 26	